


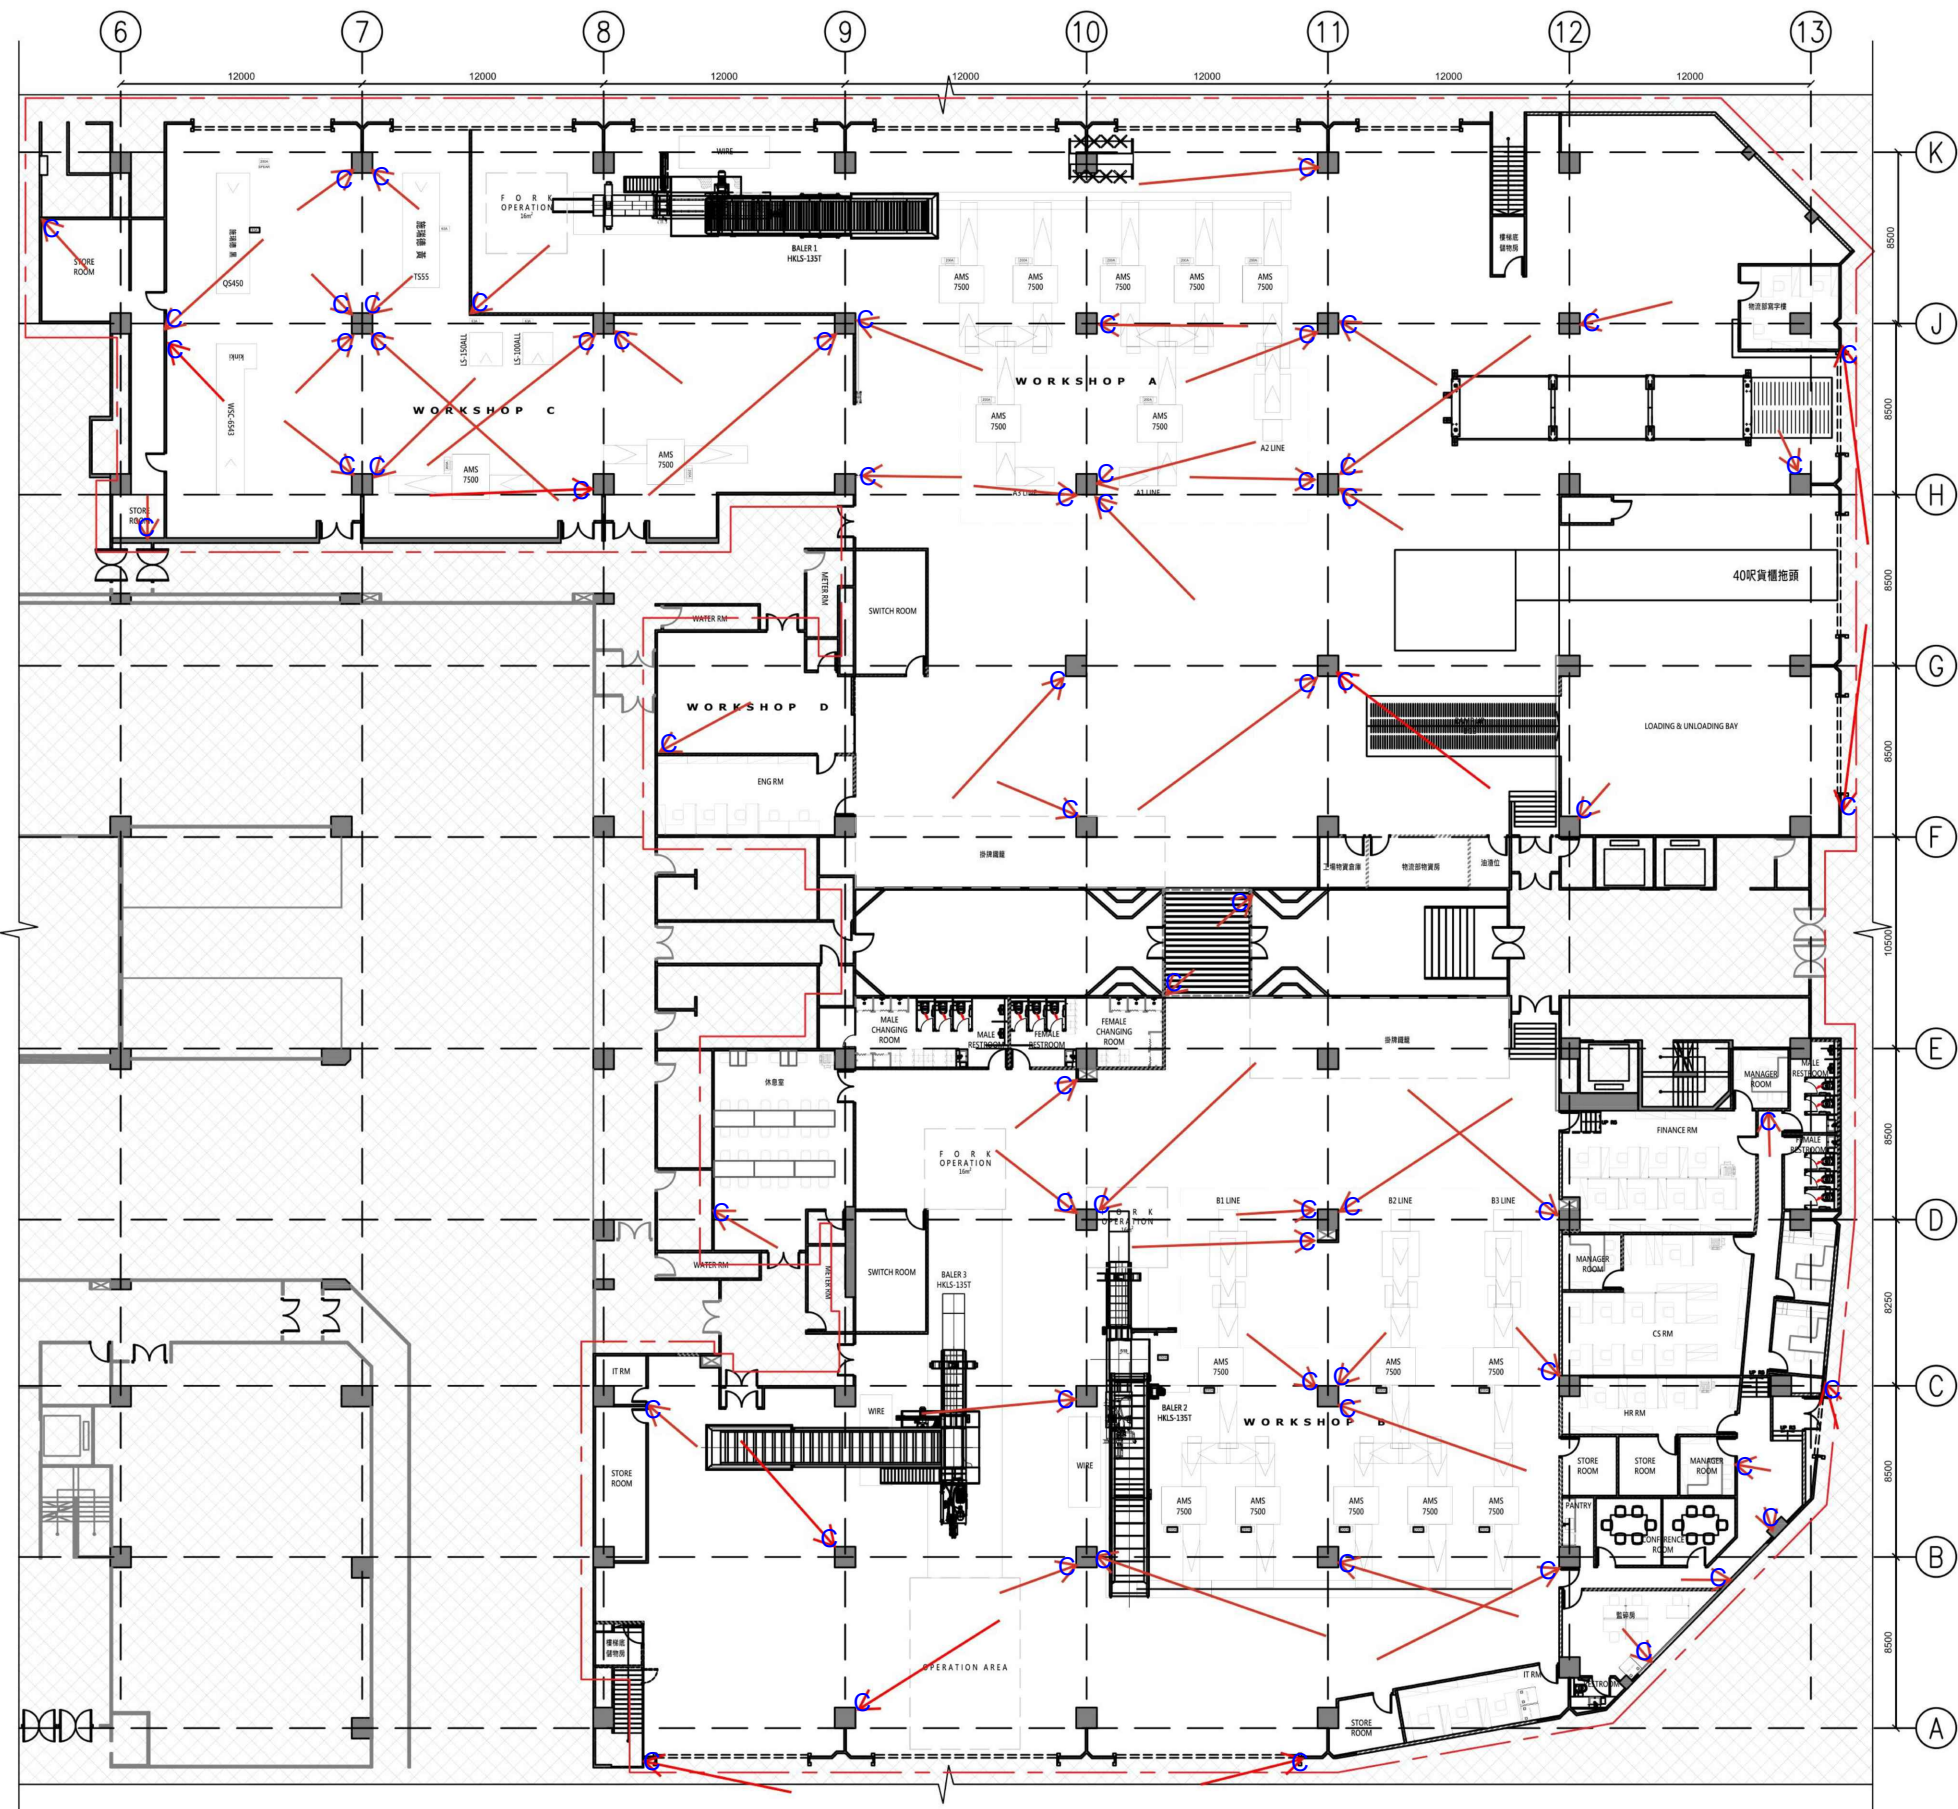

LEGEND

- SUBJECTED PERMISES
- EXISTING
- DEMOLITION WORKS
- EXISTING WALL
- P1 100mm THK. GYPSUM BOARD WALL IN WHITE PAINT FIN. UPON 3500mm AFFL.
- P2 150mm THK. SAND-CEMENT BRICK WALL IN WHITE PAINT FIN. FULL HEIGHT
- P3 100mm THK. SAND-CEMENT BRICK WALL IN WHITE PAINT FIN. FULL HEIGHT
- P4 100mm THK. SAND-CEMENT BRICK WALL IN WHITE PAINT FIN. UPON 3500mm AFFL.
- F01 10mm THK. STEEL PLATE LAY-ON THE EXISTING FLOORING
- F02 CARPET TILE
- F03 WALL-TO-WALL VINYL SHEET FLOORING MID-GREY COLOR FINISH
- C01 OPEN CEILING
- C02 600x600mm EXPOSED GRID CEILING W/. MINERAL FIBER CEILING TILE
- D1 900mm WIDTH x 2150mm HIGH SINGLE LEAF TIMBER DOOR IN PLASTIC LAMINATE FIN. W/. VISION PANEL
- D3 1570mm WIDTH x 2150mm HIGH DOUBLE LEAF CORE TIMBER DOOR IN PLASTIC LAMINATE FIN. W/. VISION PANEL
- m NEW HANG MIRROR (400mm(W) X 1300mm(H))
- NEW EXIT SIGN

DRAWING STATUS

TENDER DRAWING

CLIENT



PROJECT MANAGER

EAC Earth Architectural Consultants Limited
大地建築顧問有限公司
Unit 03, 4/F, Block A,
Focal Industrial Centre,
Hung Hom, Kowloon, HK.
T +852 2123 1498
E info@eac.com.hk
W www.eacgroup.com.hk

E&M CONSULTANT



茅氏顧問工程師(香港)有限公司

PROJECT

FITTING-OUT WORKS AT WORKSHOPS B01-B23, G/F,
JUMBO PLAZA, NO.6 CHOI FAI STREET, SHEUNG SHUI

All drawings and written materials contained herein are original and unpublished works of EAC and may not be duplicated, used or disclosed without EAC's consent.

DRAWING TITLE

GENERAL ARRANGEMENT PLAN
(SHEET 1 OF 10)

DRAFTED:	CHECKED:	DESIGNED:	REVIEWED:
UL	RM	KC	FSC

REVISION NUMBER

0

SACLE

1:350 @ A3

DATE

24/03/2026

DRAWING NO.

LAY-01